

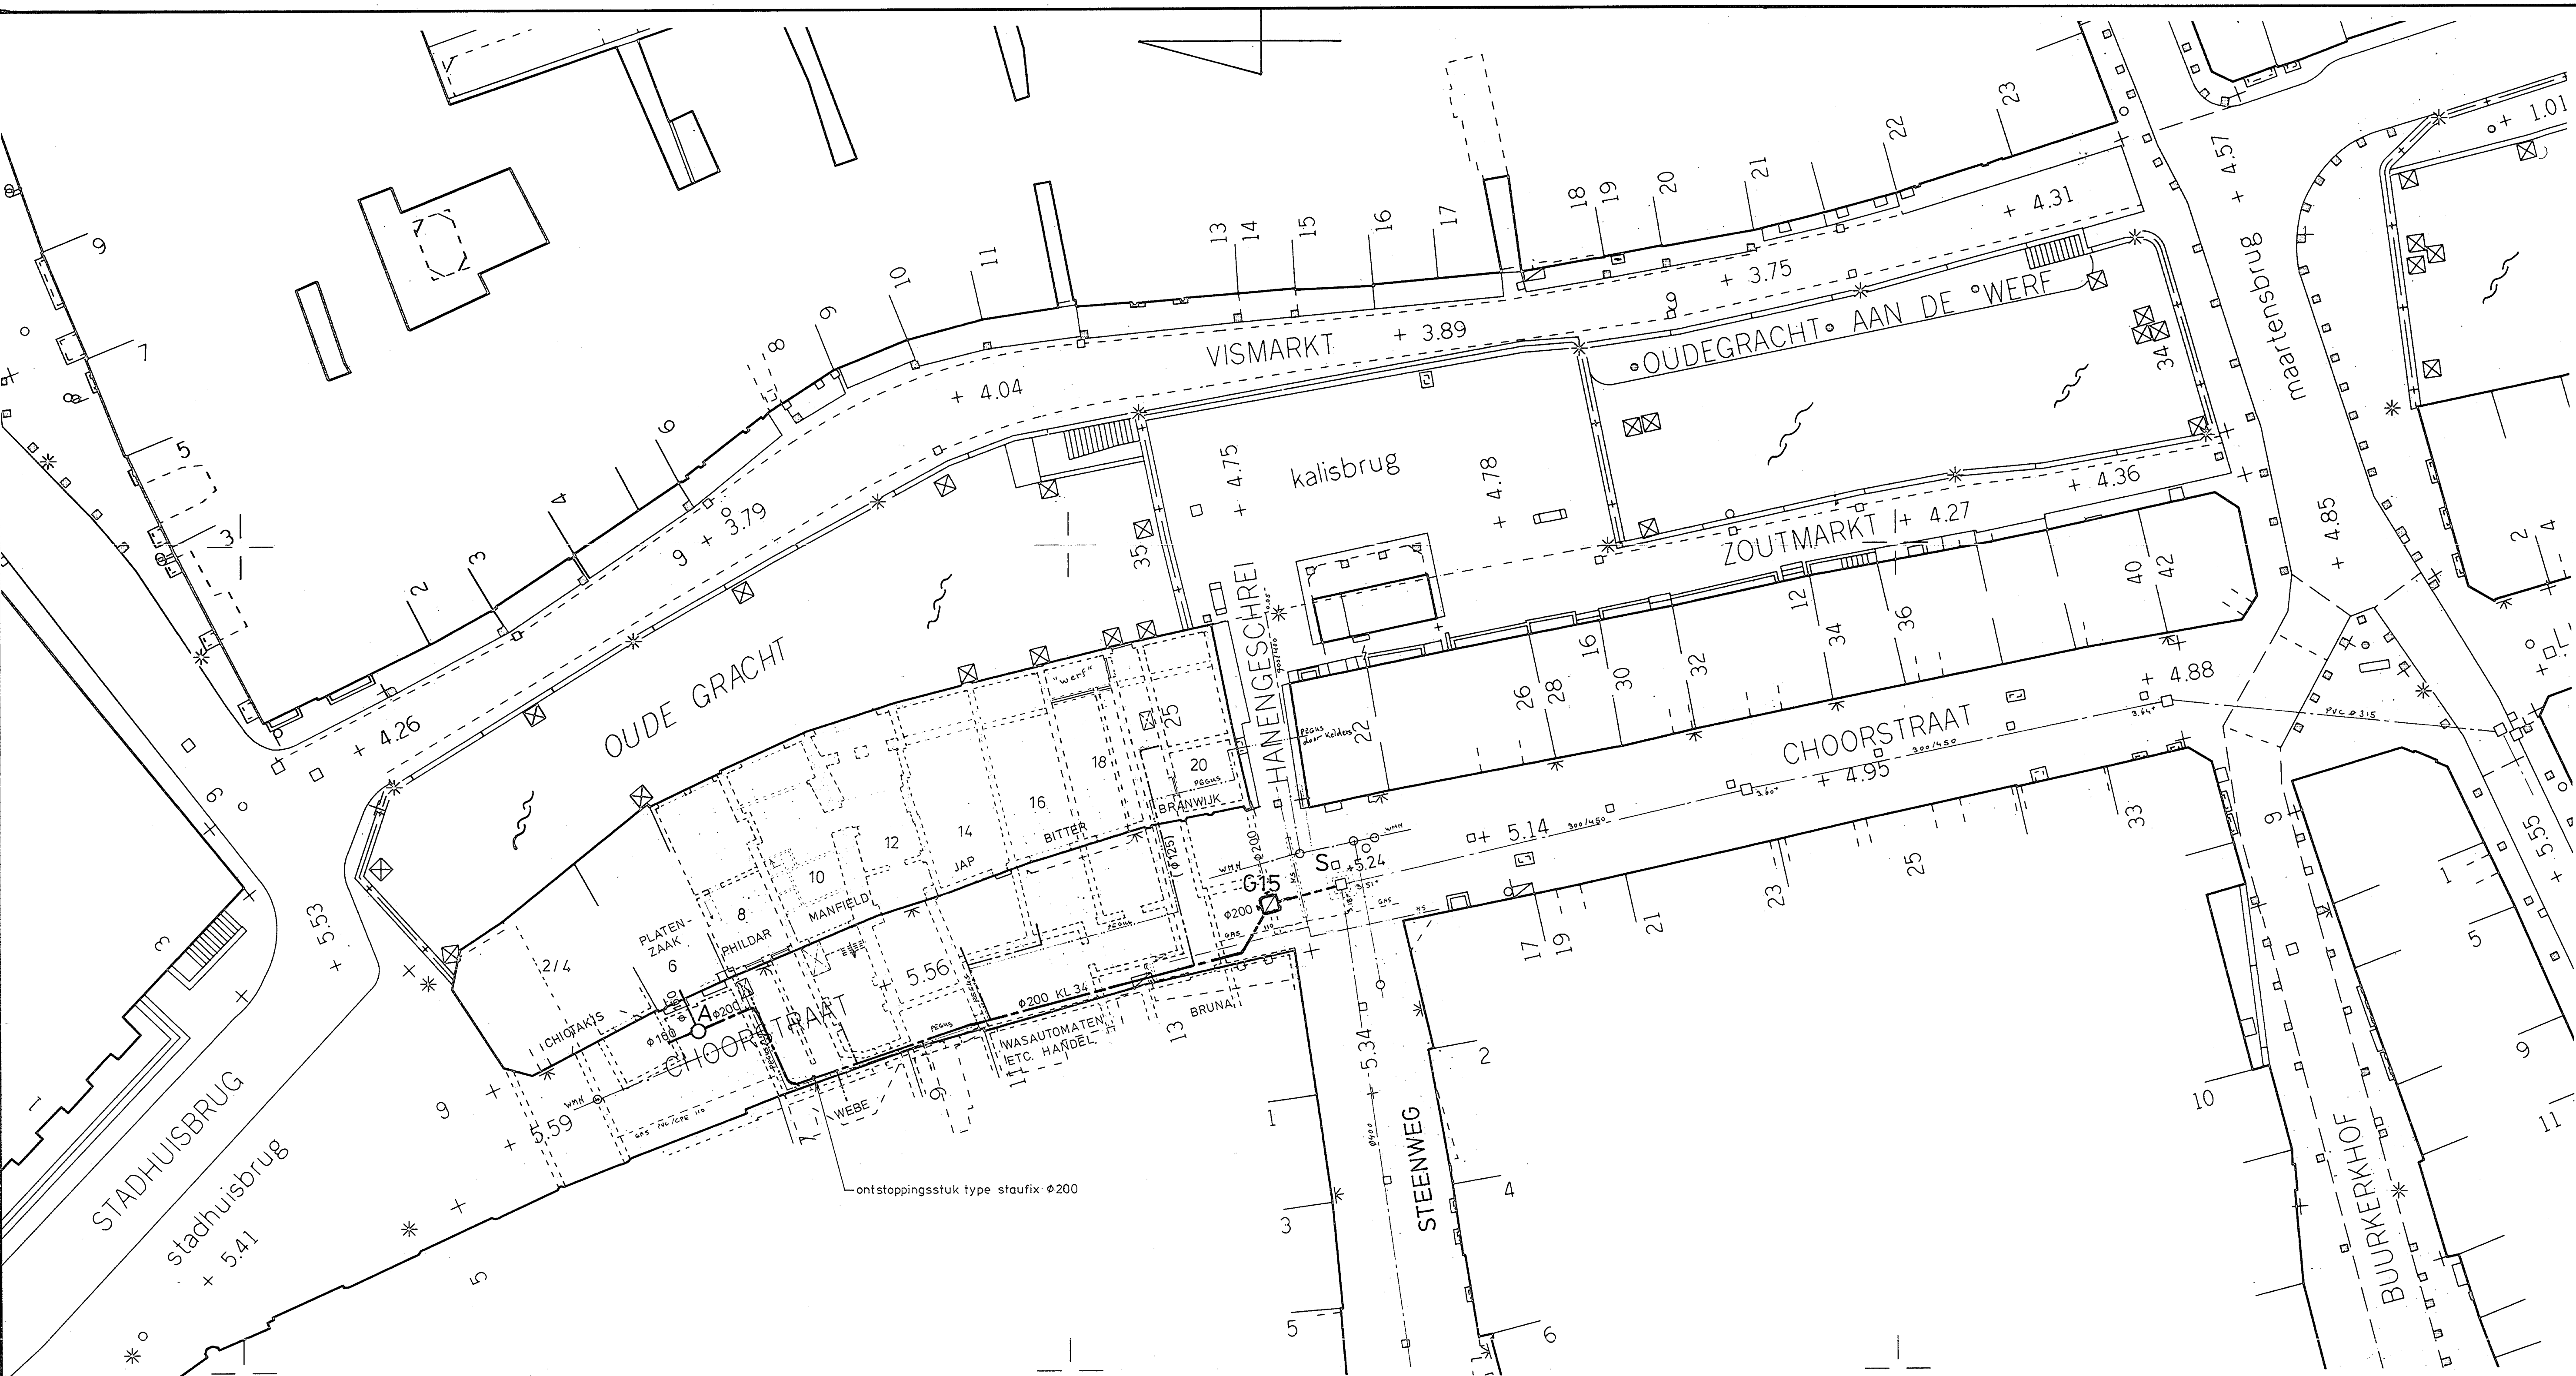


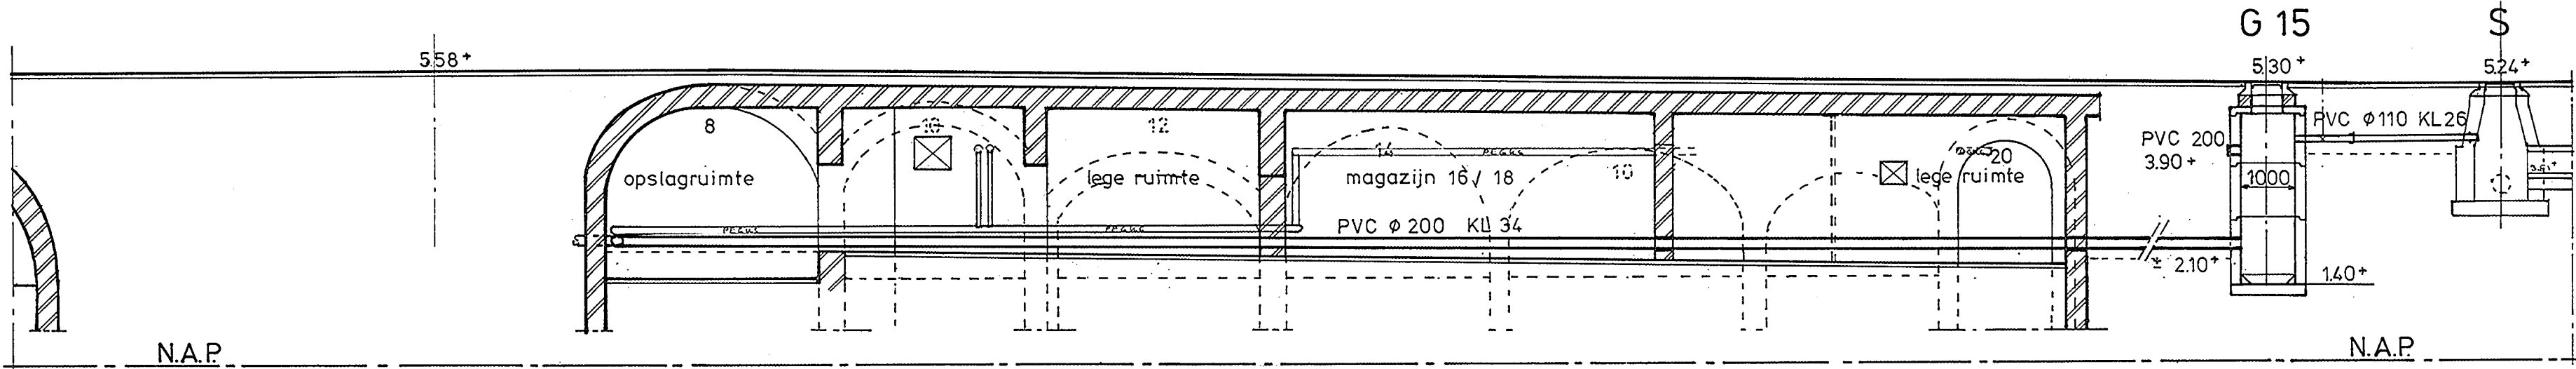

SITUATIE schaal 1:200

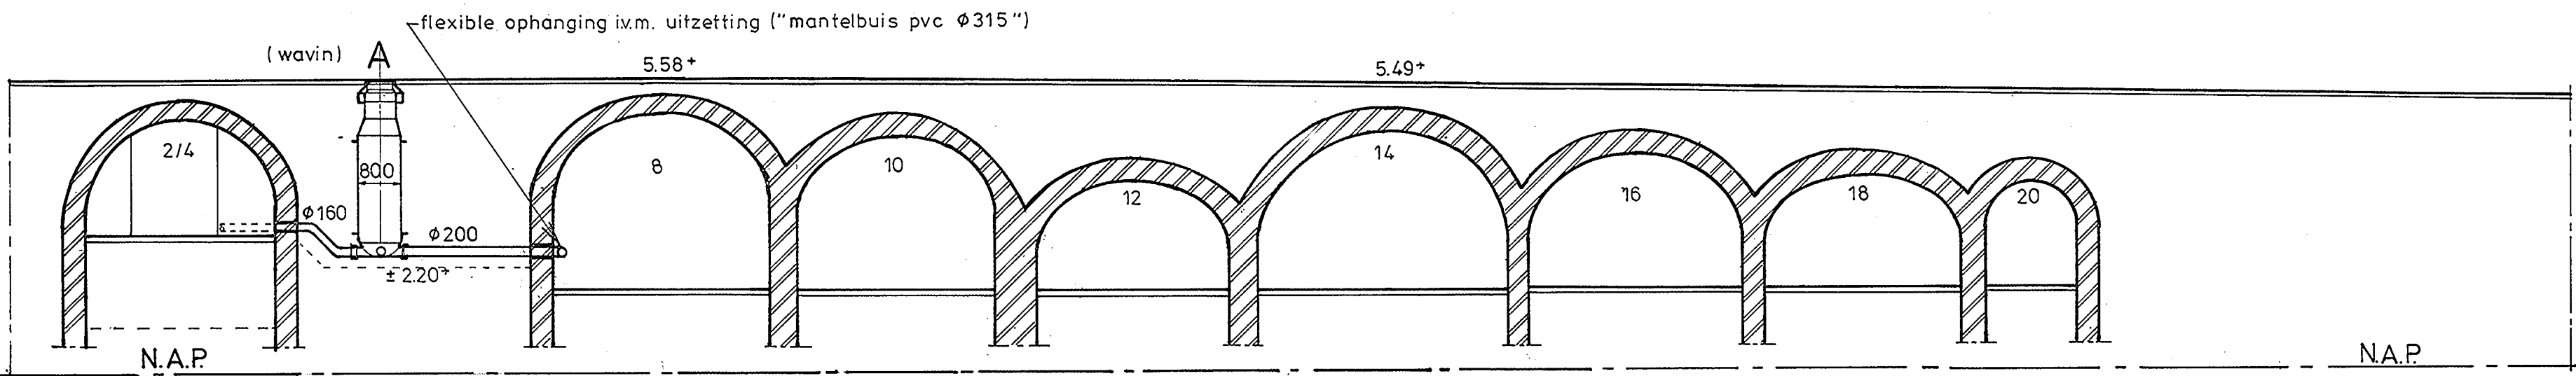

LENGTEPROFIEL schaal 1:100

HOOFDRIOL PVC Ø200 KL 34, IN DE KELDERS ONDERSTEUND MET STALEN BEUGELS VOORZIEN VAN EPOXYTEER COATING. BEUGELS H.O.H. 1 METER
AANSluit MOGELIJKHEID VOOR HUISAANSLUITINGEN D.M.V. T- STUKKEN 200/125
DE HUISAANSLUITINGEN WORDEN IN REGIE GEMAAKT
STELPOSTEN :

OPRUIMEN KELDERS f 5.000
ONVOORZIEN f 2.500

DE MAXIMAAL TOEGESTANE WIELDRUK IN DE CHOORSTRAAT IS 1 TON
DE BEVOORRADING VAN DE WINKELS MOET ALTIJD MOGELIJK ZIJN
HET TOEGESTANE VERKEER VAN MAARTENSBRUG NAAR DE STEENWEG V.V. MOET ALTIJD VRIJE DOORGANG HEBBEN

VERKLARING

- BESTAAND RIOOL MET INSPECTIEPUT: GEMENGD STELSEL
- BESTAAND RIOOL MET INSPECTIEPUT: VUILWATER
- BESTAANDE BEERPUT
- AAN TE BRENGEN RIOOL MET INSPECTIEPUT: GEMENGD STELSEL
- AAN TE BRENGEN POMPPUT MET PERSLEIDING
- AAN TE BRENGEN HUISAANSLUITING VUILWATER (IN REGIE)

- BOOM
- LICHTMAST / VERKEERSLICHT

- WATERLEIDING MET BRANDKRAAN W.M.N.
- P.E.G.U.S.- LEIDING
- GASLEIDING G.E.B./G.C.N./NED. G.A.S.U.M.I.E
- HOOGSPANNINGSKABELS G.E.B.
- LAAGSPANNINGSKABELS G.E.B.
- TELEFOONKABELS
- C.A.I. KABEL
- P.U.E.M. KABEL
- BRANDPUT c.q. PEILBUIJS

ZIE DE
LEIDINGTEKENINGEN
VAN DE
BEDRIJVEN

DE VORM EN HOOGTELIJGGING VAN DE KELDERS ZIJN NIET EXACT BEKEND
DE JUISTE MATEN IN HET WERK TE BEPALEN
ALLE MATEN IN MM TENZIJ ANDERS AANGEGEVEN
ALLE HOOGTEMATEN IN METERS T.O.V. N.A.P.

VOOR ALGEMENE DETAILS RIOLERINGSWERKEN ZIE TEK. 4766-G
JUISTE PLAATS KABELS EN/OF LEIDINGEN IN HET WERK TE BEPALEN

DIENSTENSTRUCTUUR R.O.V.U.		Ravetlaan 96, UTRECHT	
DIENST OPENBARE WERKEN		Afd. Riol. en Waterhuish.	
WERK	HET UITVOEREN VAN RIOLINGSWERKEN, RIOLERINGSWERKEN EN VERHARDINGSWERKEN IN DE CHOORSTRAAT TUSSEN STEENWEG EN STADHUISBRUG.		BESTEK 54 O.W. 1988
OMSCHR.	SITUATIE, LENGTEPROFIELEN EN DETAILS		GEZ.
SCHAAL 1:200 1:100	GET.	GEZ.	FORMAAT 105x75 20-II 15.350-1